
✦ KRYPTA · EKKLESIA · A3 ARKKITEHTUURIKARTTA (1 M = 10 PX) ✦

PYHÄN VELKAVANKIFLAGELANTIN LUOSTARI

III · 2. kerros: Suuri makuusali, Kokelaiden sali, Lähetys- ja kirjurinsali, Vanhimmat & Vierassiipi

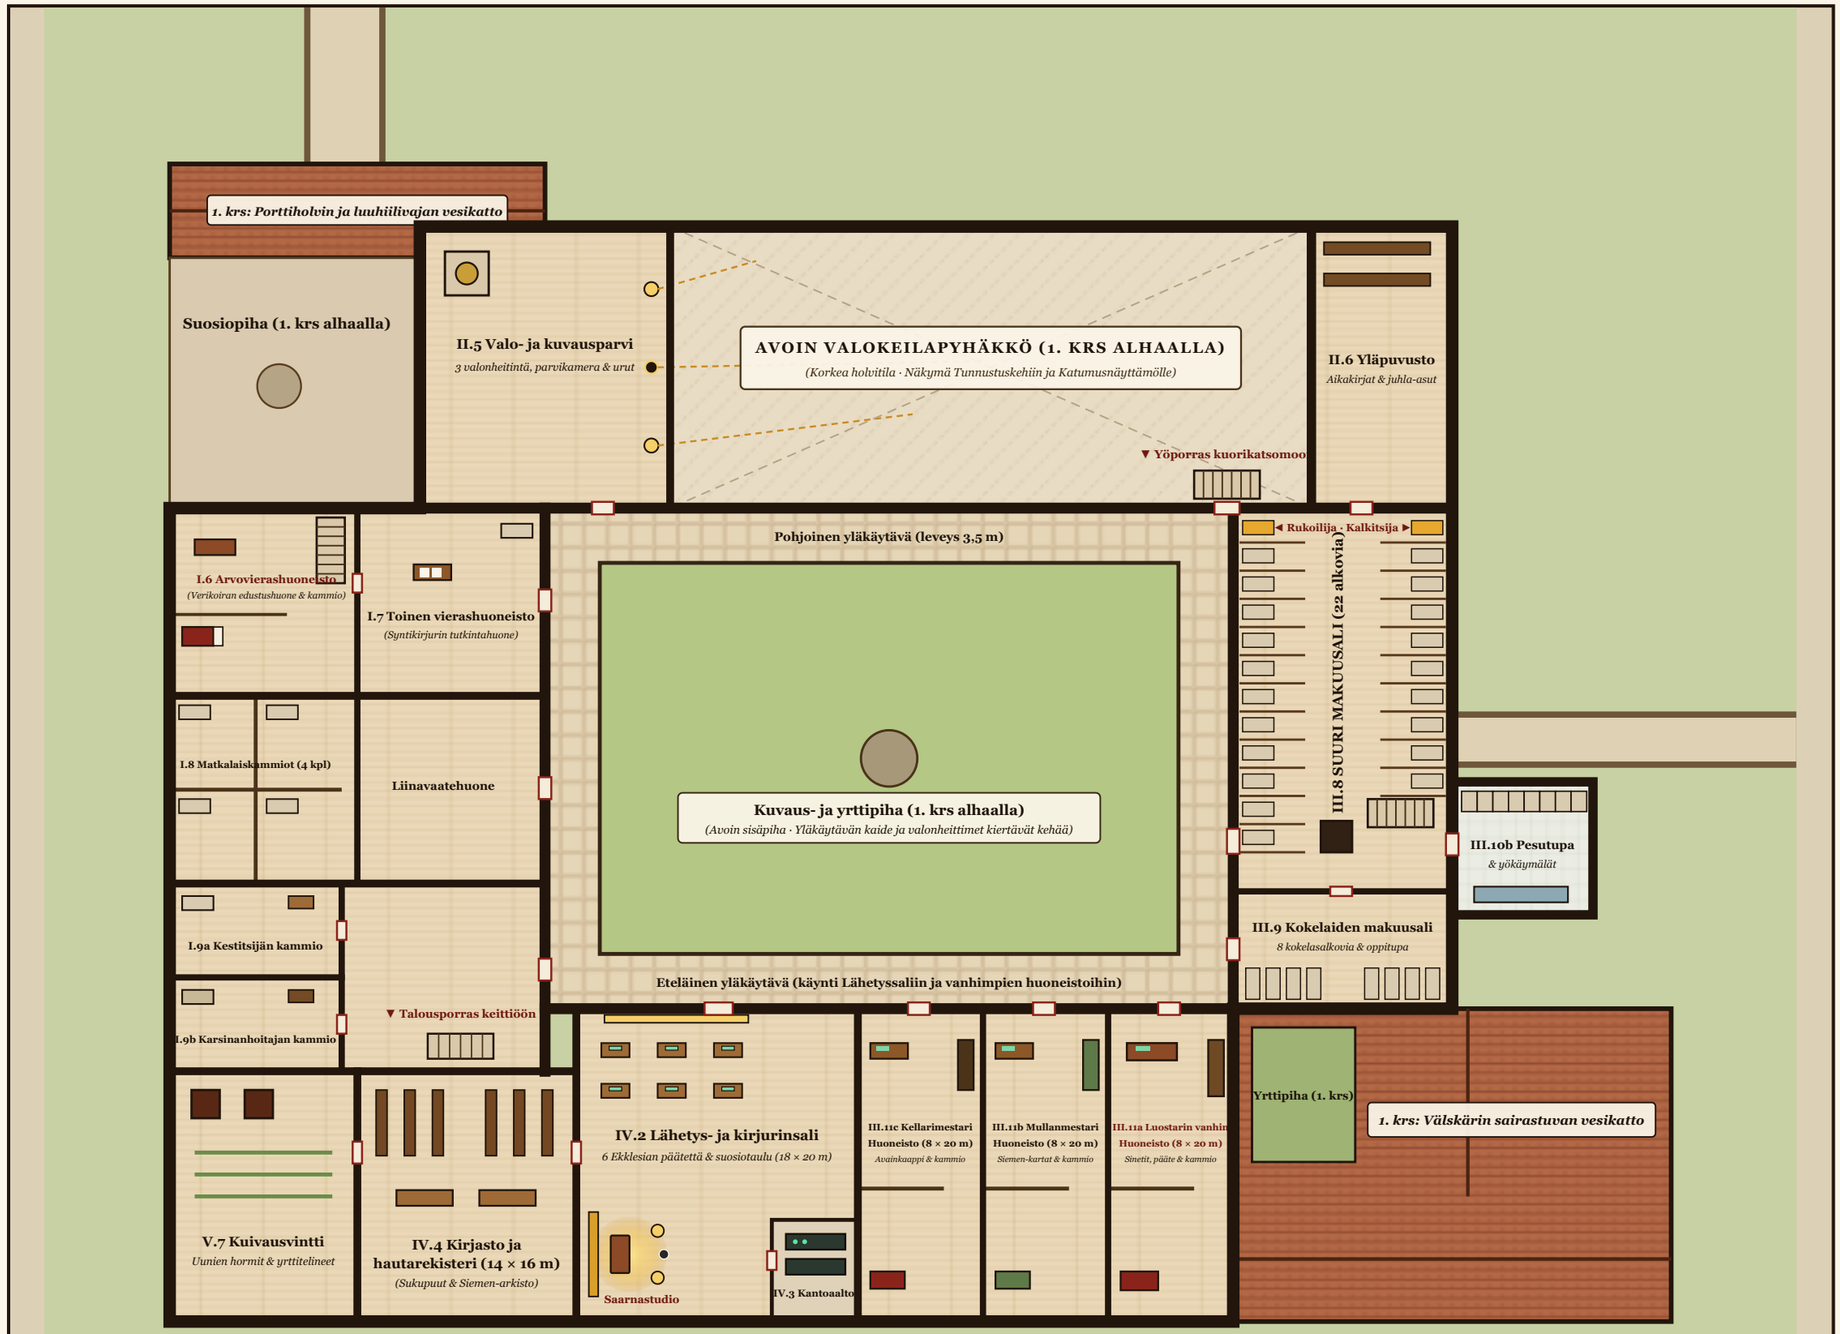

VYÖHYKE III · SUURI MAKUUSALI JA KOKELAIDEN SALI

III.8 Suuri makuusali `(14 × 24,5 m)` — 22 matalilla puuväliseinillä erotettua makuualkovia (kukin `4,2 × 1,8 m`, vuode `0,9 × 2,0 m`). Ekklesiassa rivimunkilla ei ole lukittua ovea: suoraan *Yöportaan* suulla ovat **Sokean Rukoilijan alkovi** ja **Kalkitsijan alkovi**.

III.9 Kokelaiden makuusali `(14 × 7,5 m)` — 8 nuoren kokelaan makuualkovit ja oppitupa makuusalin eteläpäässä.

III.10b Yläkerran pesutupa ja yökäymälät `(9 × 8,5 m)` — 8 käymälää ja aamupesuallas suoraan makuusalin kyljessä.

VYÖHYKE III.11 · LUOSTARIN VANHIMPIEN HUONEISTOT

Kolmen pelaajamunkin tilavat, kaksiosaiset yksityishuoneistot (työhuone + makuukammio, kukin `8 × 20 m = 160 m²`), joihin kamerat eivät ulotu:

III.11a Luostarin vanhimman huoneisto — Edustuspöytä, luostarin sinetit, verkkopääte ja yksityinen makuukammio.

III.11b Mullanmestarin huoneisto — Siemen-aseman kartat, maaperänäytteet, peltokoneiden ohjauspääte ja makuukammio.

III.11c Kellarimestarin huoneisto — Vainajakirjanpito, lukittu avainkaappi (sis. Katakombiportin vara-avaimen), lääkintäkaappi ja makuukammio.

VYÖHYKE IV · LÄHETYSSALI, KANTOAALTO JA KIRJASTO

IV.2 Lähetys-, leikkaus- ja kirjurinsali `(18 × 20 m)` — **6 Ekklesian tietokonepäätettä** `(1,6 × 0,8 m` pöydät) videoiden leikkaukseen, paimenblogin päivitykseen ja kommenttien moderointiin, seinällä **suosiomittaritaulu** sekä **Saarnastudio** (kultatausta, rengasvalot ja kamera).

IV.3 Kantoaalto- ja palvelinhuone `(5,5 × 6,5 m)` — Lukittu lähetinholvi Kuiskauksen ja Ikonin verkkoihin.

IV.4 Kirjasto ja hautarekisteri `(14 × 16 m)` — Reseptikirjat sekä Kryptan sukupuu- ja kuolinrekisterit.

V.7 Lämmin kuivausvintti `(12 × 16 m)` — Leipomon luuhiiliuunien hormien lämmittämä yrtti- ja pellavavintti.

VYÖHYKE I & II · VIERASSIIPI JA VALOPARVI

I.6 Arvovierashuoneisto (Verikoira) `(12 × 12 m)` — Jahtikommodori Valkohanskaisen Verikoiran edustushuone ja makuukammio.

I.7 Toinen vierashuoneisto (Syntikirjuri) `(12 × 12 m)` — Haaskalintujen Syntikirjurin majoitus ja pahvikansioiden tutkintahuone.

I.8 Matkalaiskammiot (4 kpl) & Liinavaatehuone — Saattueiden yöpymishuoneet.

I.9a–b Kestitsijän ja Karsinanhoitajan kammiot `(2 × 11 × 6 m)` — Vastuumunkkien omat huoneet talousportaan äärellä.

II.5–6 Valo- ja kuvausparvi & Yläpuvusto — 3 valonheitintä, parvikamera, kelloköydet sekä juhla-asu- ja aikakirjaholvi.

MITTAKAAVA 1 : 100 (1 m = 10 px · Makuualkovi = 4,2 × 1,8 m)

0 — 5 m — 10 m — 20 m — 30 m

Yhteensä 30 makuu- ja kokelasalkovia + 7 erillistä kammiohuoneistoa